


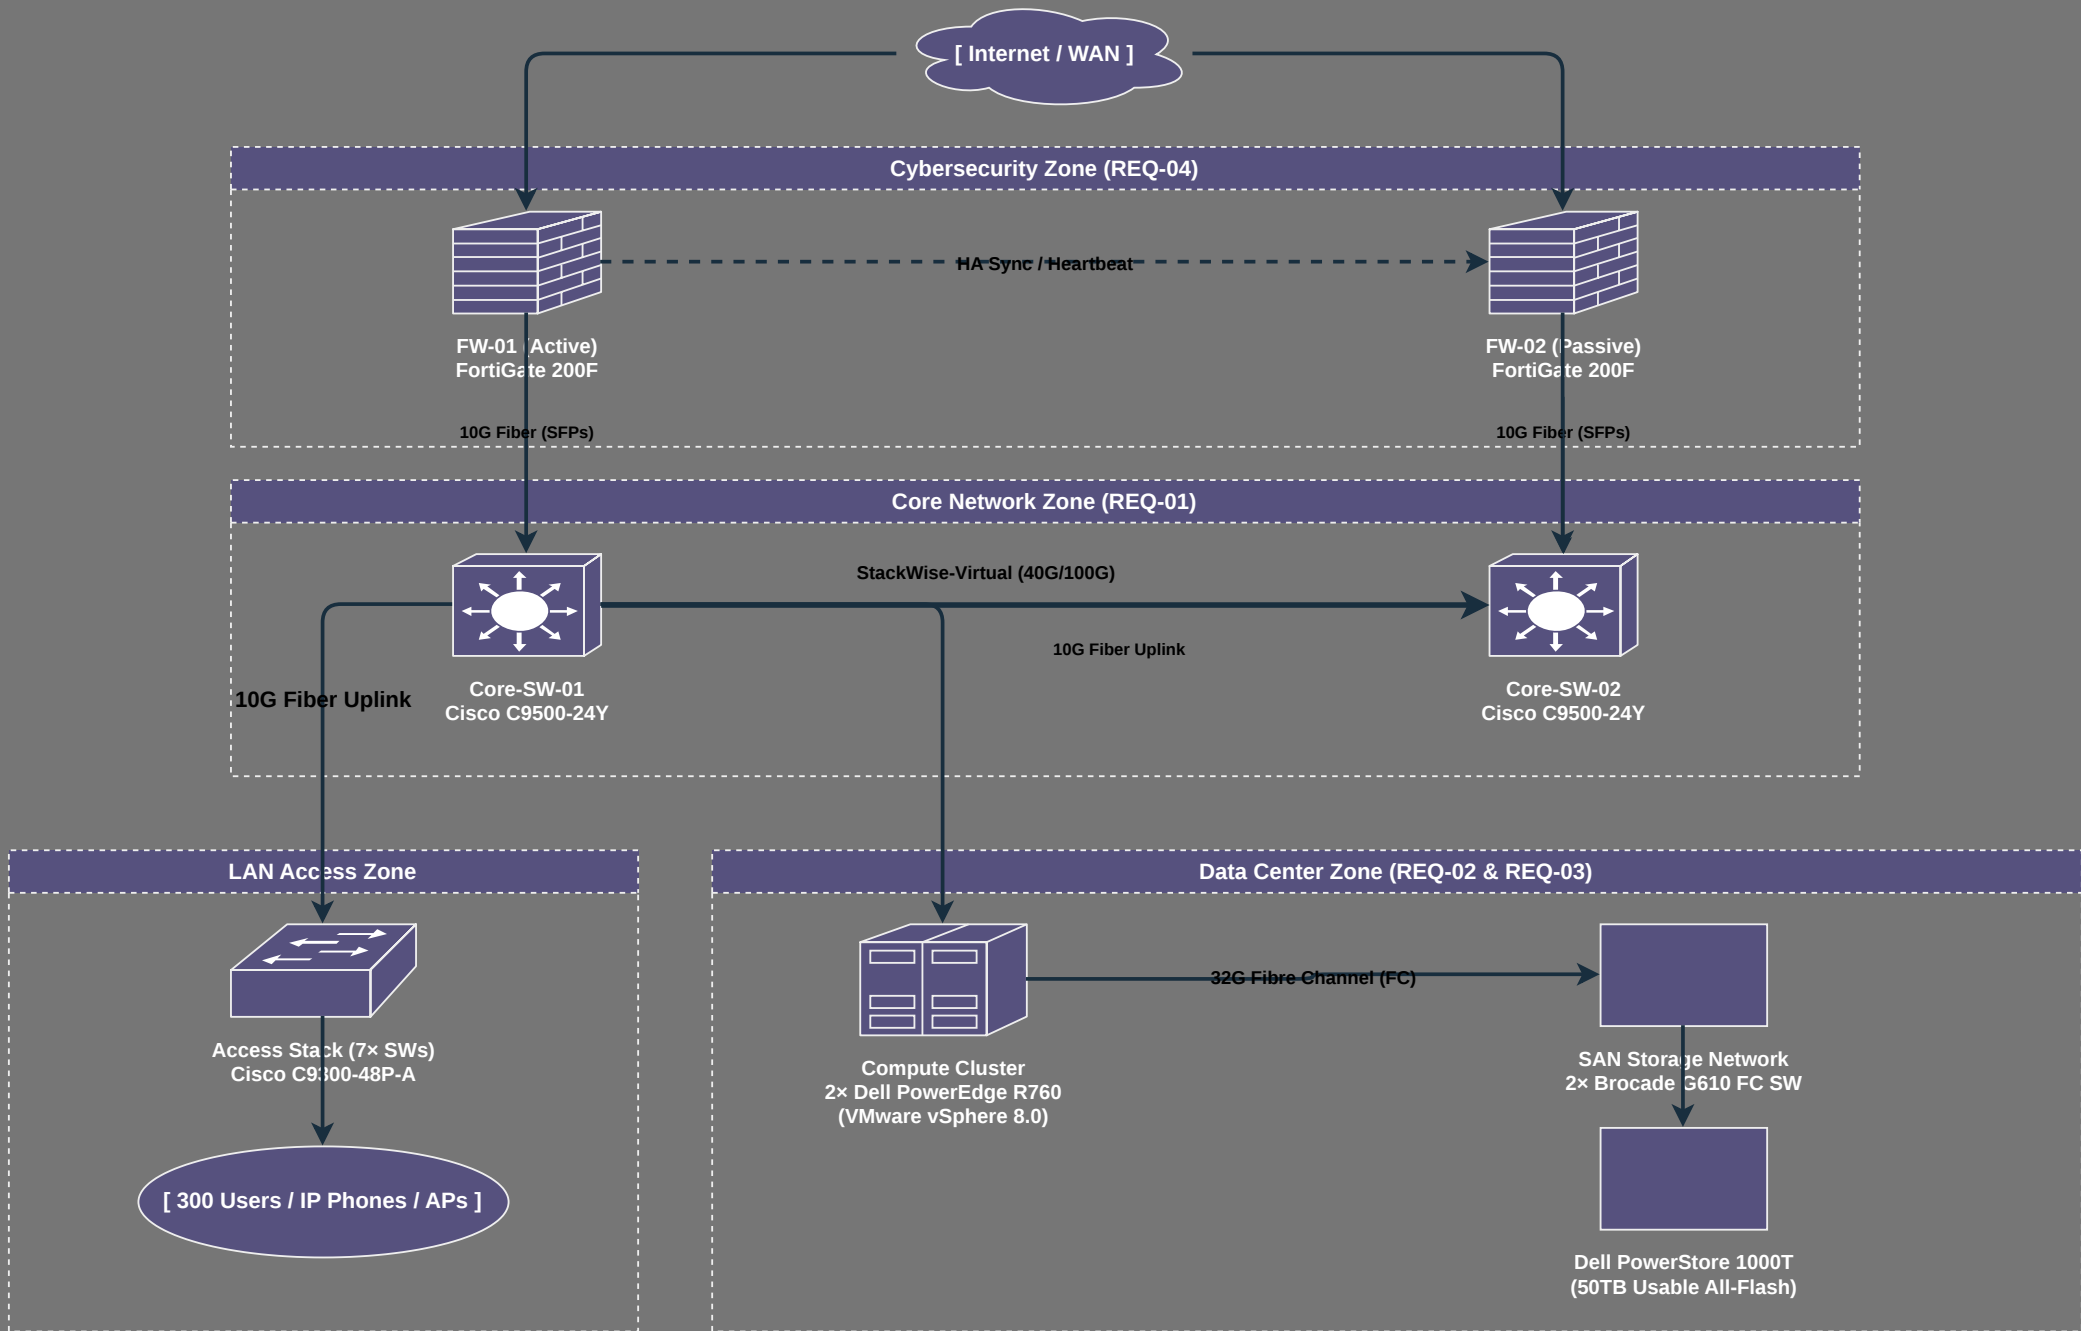

Main Server Cabinet (42U Rack - DC Room)

U40-U42: Fiber Tray & Cat6A Patch Panels (Core Uplinks)

U38: FortiGate 200F (FW-01 Primary)

U36: FortiGate 200F (FW-02 Secondary HA)

U34: Cisco Core C9500-24Y (Core-SW-01)

U32: Cisco Core C9500-24Y (Core-SW-02)

U30: Brocade G610 FC Switch (SAN-SW-01)

U28: Brocade G610 FC Switch (SAN-SW-02)


U23-U24 (2U): Dell PowerEdge R760 (ESXi Host 01)

U20-U21 (2U): Dell PowerEdge R760 (ESXi Host 02)


U12-U15 (4U): Dell PowerStore 1000T SAN Array (50TB All-Flash Storage)

U01-U06 (6U): Smart-UPS Online 6000VA / Dual Redundant PDU Units


1st Floor: Administrative & Executive HQ Zone

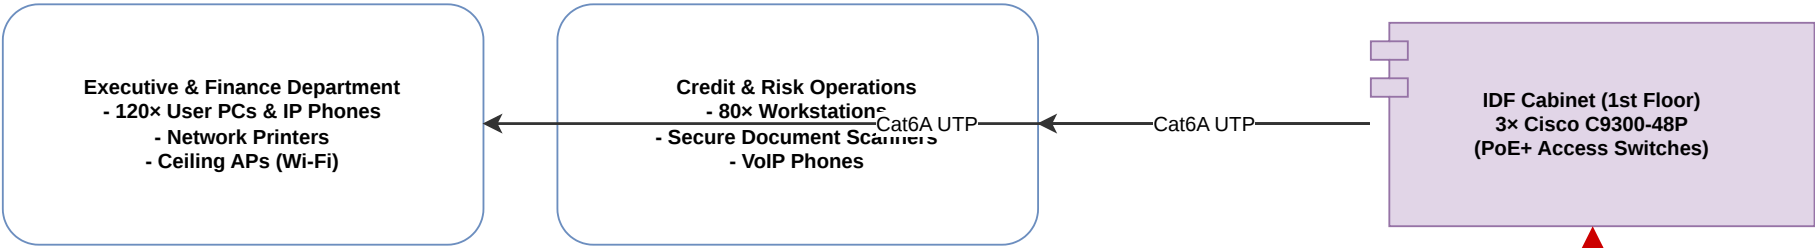

Ground Floor: Retail Banking & Customer Operations Zone

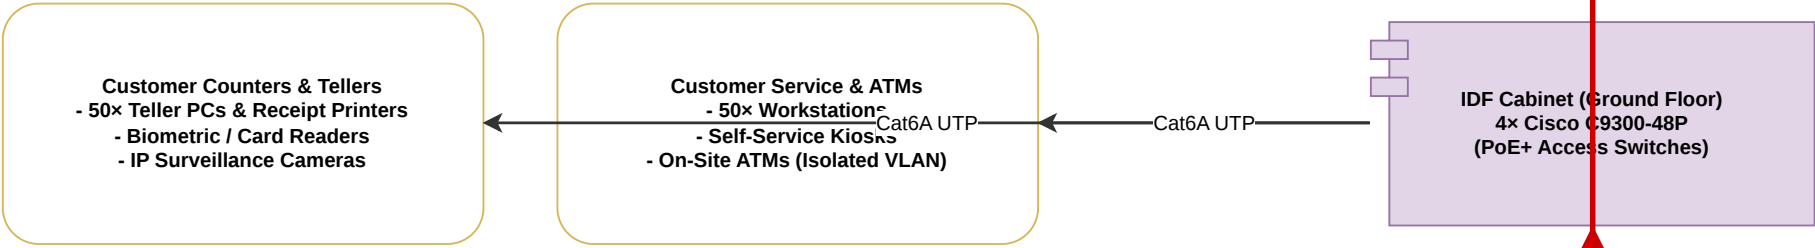

Basement Floor: Main Data Center (MDF Room - REQ-01/02/03/04)

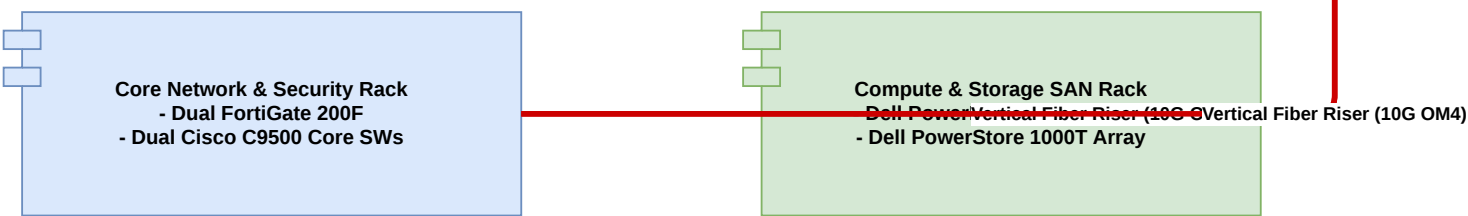

Core Security & Routing Layer (802.1Q Trunking)

Core Switches & FortiGate Firewalls
(Inter-VLAN Routing & Security Inspection)

802.1Q Trunk

802.1Q Trunk

802.1Q Trunk

802.1Q Trunk

802.1Q Trunk

VLAN 10: Management
Subnet: 10.10.10.0/24
- Switches & Firewalls
- ESXi & Storage Mgmt

VLAN 20: Tellers & Retail
Subnet: 10.10.20.0/24
- Teller Workstations
- Receipt Printers

VLAN 30: HQ Administration
Subnet: 10.10.30.0/23
- Executive PCs
- Finance & Credit Staff

VLAN 40: Voice (VoIP)
Subnet: 10.10.40.0/24
- IP Phones
- Voice Gateway

VLAN 60: ATM Network
Subnet: 10.10.60.0/24
- On-Site & Off-Site ATMs
- Isolated IPsec Tunnel

Firewall High Availability Zone (Active / Passive Failover)



Core Switch Redundancy Zone (StackWise-Virtual High Availability)



Compute & SAN Storage Dual Multipathing Redundancy

